



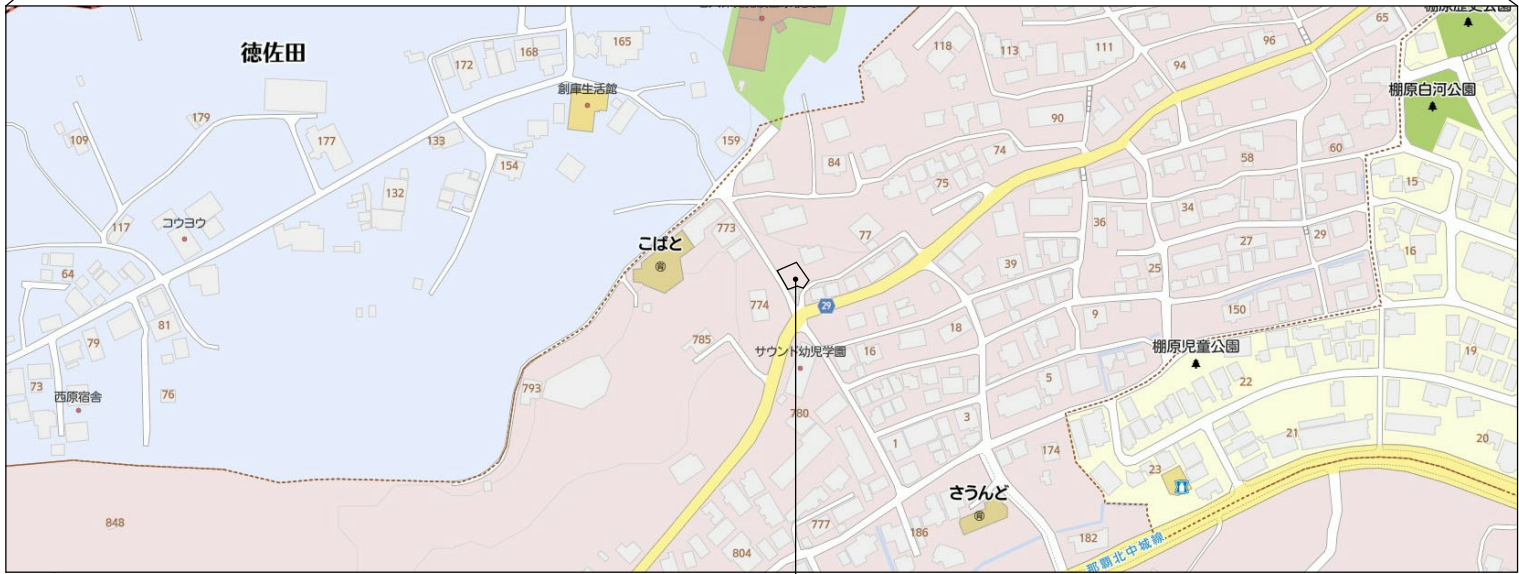

申請地：沖縄県西原町字棚原81-4

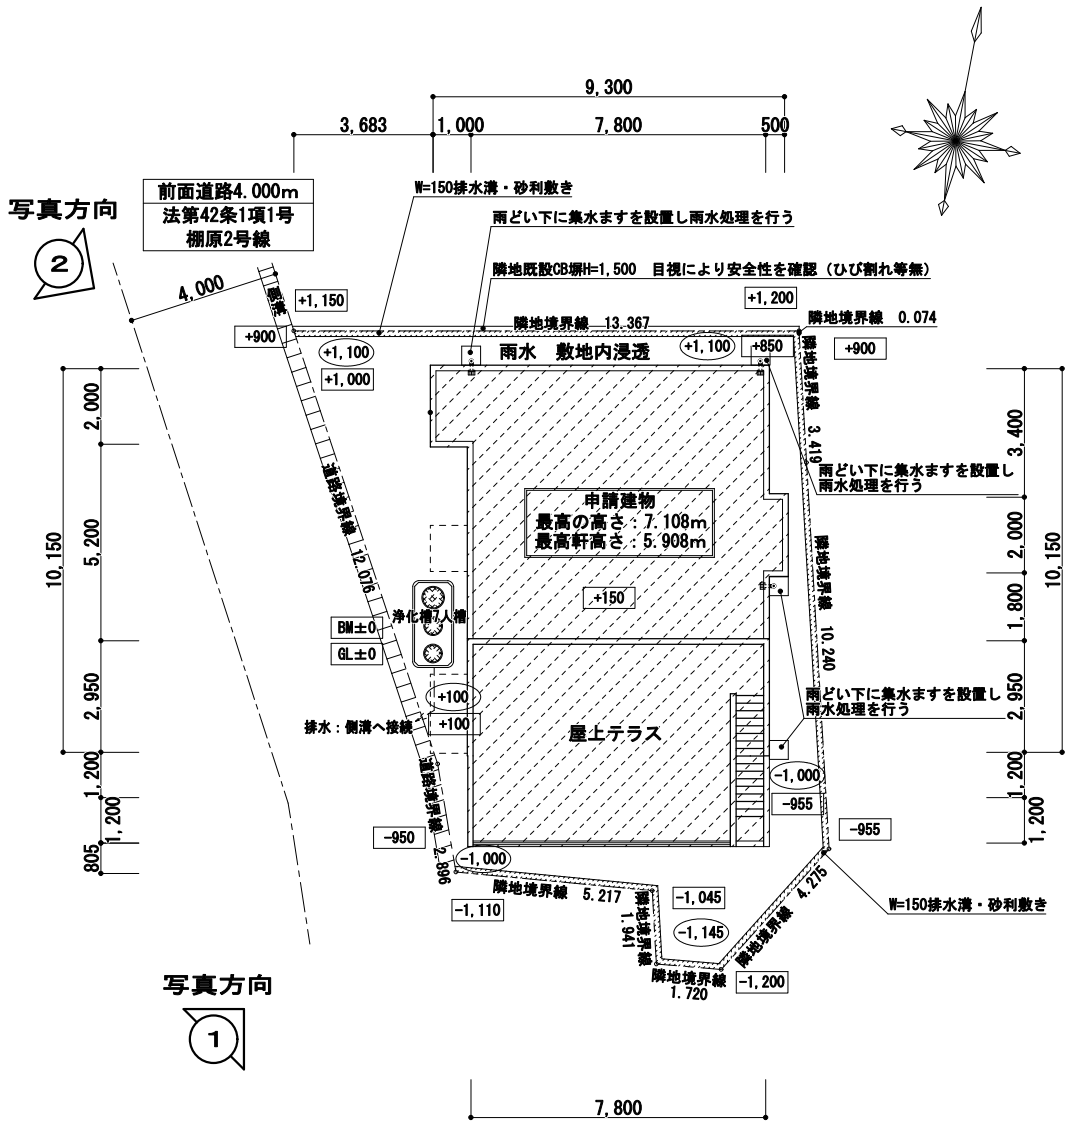

	現況レベル
	設計計画レベル

 一級建築士事務所 アトリエ かなえ	〒901-0405 沖縄県八重瀬町字伊瀬122-3-A 沖縄県知事登録 第162-3951号 TEL 098-998-1566 / FAX 098-998-1567	一級建築士登録 第 350958 号 漢那 晋苗	DWG. DATE 2025/12/24 PRINT. DATE 令和8年 7月16日	検図	製図	縮尺 S=1/200	工事名称	儀保様住宅新築工事	施主印	図面番号 A -101
							図面名称	案内図・配置図		