


敷地求積図

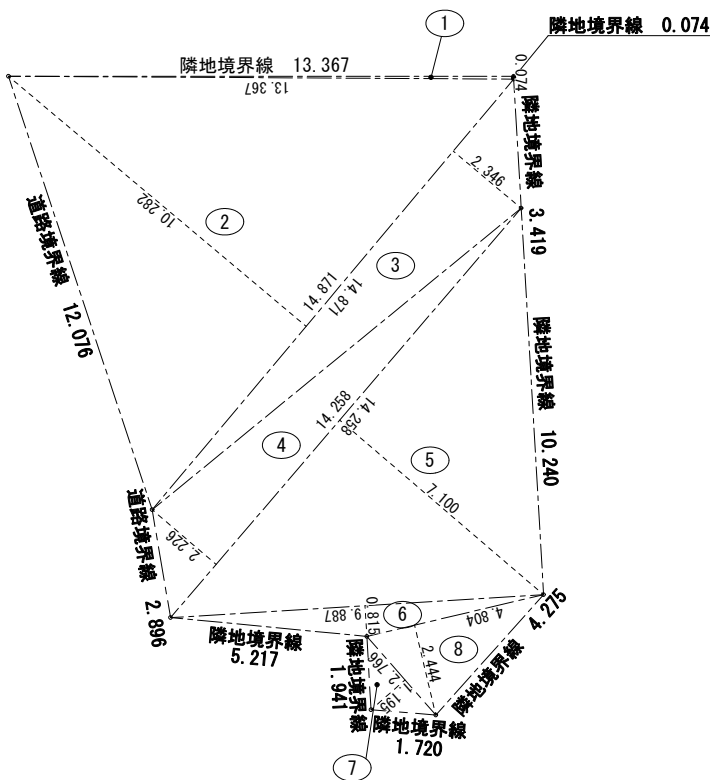


番号	底 辺	高 さ	倍 面 積	面 積
1	13.367	0.074	0.989158	0.4945790
2	14.871	10.282	152.903622	76.4518110
3	14.871	2.346	34.887366	17.4436830
4	14.258	2.226	31.738308	15.8691540
5	14.258	7.100	101.231800	50.6159000
6	9.887	0.815	8.057905	4.0289525
7	2.766	1.195	3.305370	1.6526850
8	4.804	2.444	11.740976	5.8704880
合 計				172.4272525
敷 地 面 積				172.42 m ²

建蔽率・容積率算定

敷地面積	172.42 m ² (52.15 坪)	建ぺい率 (指定建ぺい率 60.00 %)
建築面積	93.09 m ² (28.15 坪)	93.09 / 172.42 × 100 = 53.99 %
1 階床面積 居室部分	79.17 m ² (23.94 坪)	判定 53.99 % < 60.00 % O K
2 階床面積 居室部分	85.29 m ² (25.80 坪)	
床面積合計	164.46 m ² (49.74 坪)	容積率 (指定容積率 150.00 %)
		164.46 / 172.42 × 100 = 95.38 %
床面積合計 (法的)	164.46 m ² (49.74 坪)	判定 95.38 % < 150.00 % O K

建築面積・延べ面積

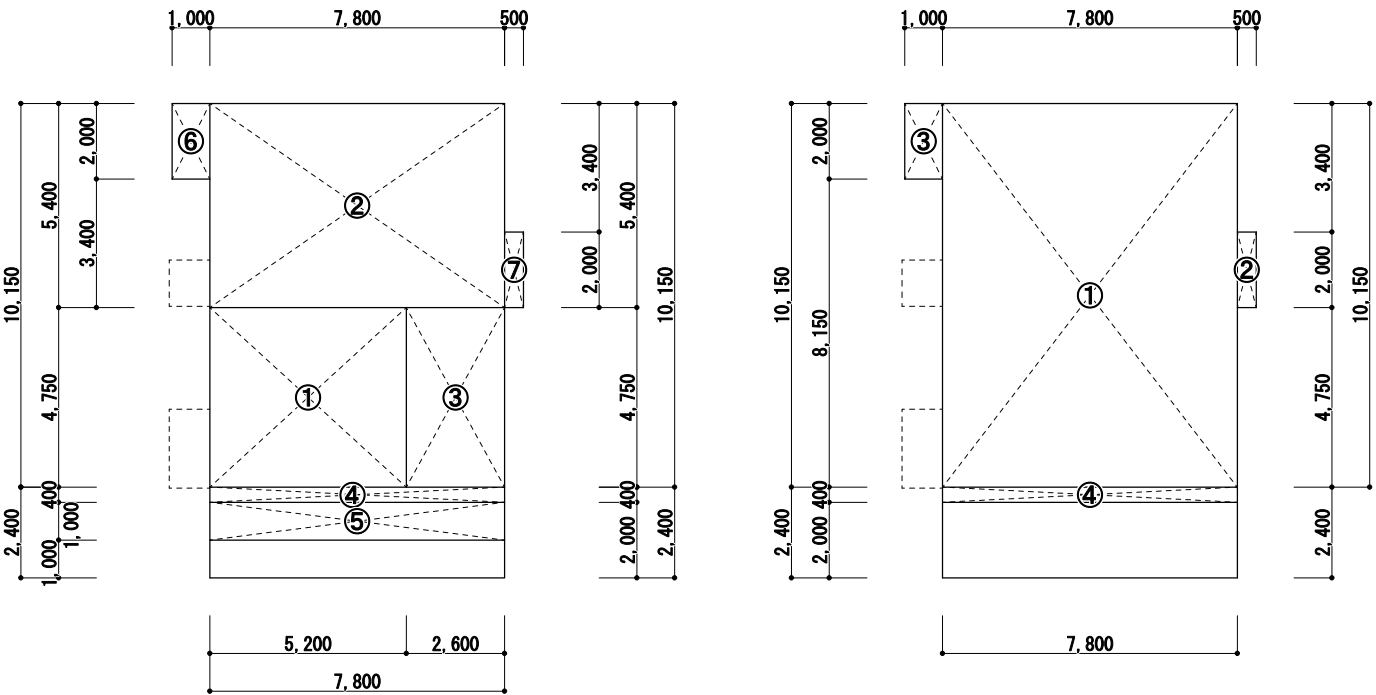

1階平面図 S=1/200

2階平面図 S=1/200

建築面積			
	計算式		面積
①	5.200 ×	4.750	24.70
②	7.800 ×	5.400	42.12
③	2.600 ×	4.750	12.35
④	7.800 ×	0.400	3.12
⑤	7.800 ×	1.000	7.80
⑥	1.000 ×	2.000	2.00
⑦	0.500 ×	2.000	1.00
			93.09

1 階			
	計算式		面積
①	5.200 ×	4.750	24.70
②	7.800 ×	5.400	42.12
③	2.600 ×	4.750	12.35
面積計(m ²)			79.17

2 階			
	計算式		面積
①	7.800 ×	10.150	79.17
②	0.500 ×	2.000	1.00
③	1.000 ×	2.000	2.00
④	7.800 ×	0.400	3.12
面積計(m ²)			85.29

事務所		
	計算式	
①	5.200 ×	4.750
		24.70
		24.70

延べ面積：164.46㎡ 事務所面積：24.70㎡
延べ面積：164.46/2=82.23㎡ > 事務所面積：24.7㎡
事務所面積は50㎡以下、延べ面積の1/2未満である



一級建築士事務所
アトリエ かなえ

〒901-0405 沖縄県八重瀬町宇伊覇122-3-A
沖縄県知事登録 第162-3951号 TEL 098-998-1566 / FAX 098-998-1567

一級建築士登録 第 350958 号
漢那 香苗

DWG. DATE
2025/12/04
PRINT. DATE
令和8年 7月16日

検図

製図

縮尺
S=1/200

工事名称

備保様住宅新築工事

施主印

図面番号

図面名称

面積表

A - 103