


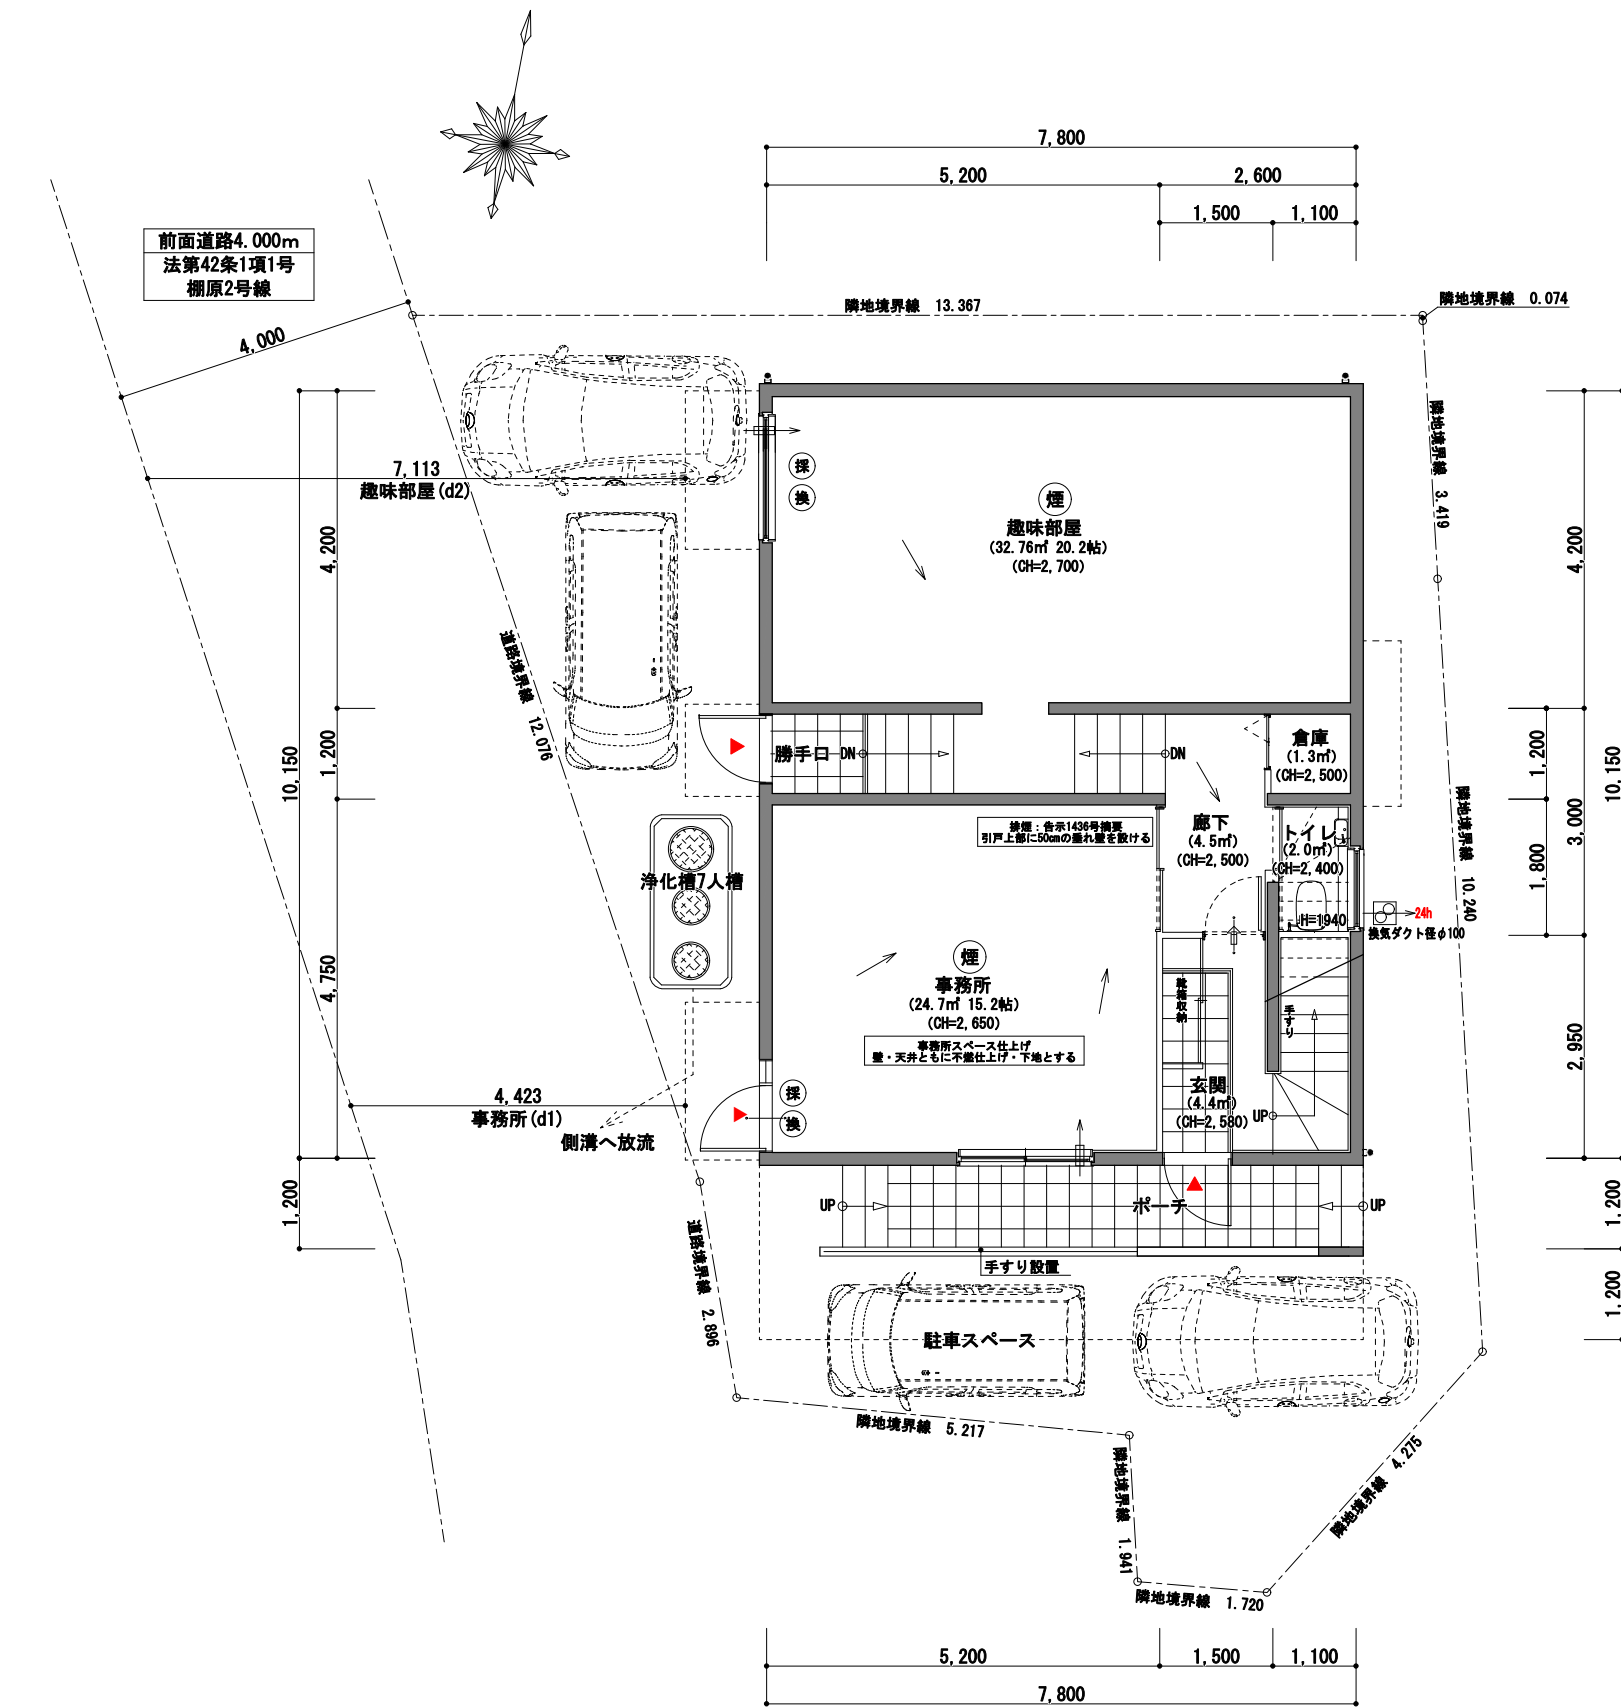

採光計算表(1階)

趣味部屋									
7.800	×	4.200	=	32.76	㎡				
32.76	／	7.00	=	4.68	㎡				
水平距離 D2=	7.113	A=	3.00						
垂直距離 H2=	4.100								
7.113	／	4.1	×	6	-	1.4	=	9	
1.65	×	1.0	=	1.65	㎡				
3.00	×	1.65	=	4.95	㎡				
4.95	≧	4.68	…	OK					

換気計算表(1階)

室名	事務所						趣味部屋					
必要換気面積	24.70	／	20	=	1.23	㎡	32.76	／	20	=	1.63	㎡
有効換気面積	2.03	*	1	=	2.03	㎡	1.65	*	1.0 * 1	=	1.65	㎡
判定	2.03	≧	1.23	…	OK		1.65	≧	1.63	…	OK	

※建具①:45°以上解放 0.884(開口部)*2.3(建具高)= 2.03

※建具45°以上解放

設備	名称	型
換気扇	天井埋込形換気扇	FY-17C8
冷暖房	霧ヶ峰GVシリーズ	MSZ-GV5625S
給湯器	エコジョーズ	RUF-E1615AG(B)

内部階段(mm)	
蹴上げ	176
踏み面	250
階段幅	890

■排煙設備の検討(1階事務所)
100㎡以下で壁・天井共に不燃仕上げであることから除外する。
告示1436号第4号ニ(4)

凡例	
●煙	住宅用火災報知機(煙式)
●熱	住宅用火災報知機(熱式)
→	換気口
→	換気扇(常時作動) 95m³/h
→	換気経路
→	アンダーカット 1cm

関係規定についての遵守事項

- ・住宅用警報機については消防法第9条、9条の2による火の使用に関する市町村条例及び住宅用防災機器の設置に関すること
- ・給水設置については水道法16条による給水措置の構造および材質に関すること
- ・液化ガス(LPG)については液化石油ガスの保安の確保及び取引の適正化に関する法律第38条の2による供給設備等の基準適合義務に関すること
- ・浄化槽については浄化槽法第3条の2第1項による浄化槽によるし尿処理等に関すること
- ・地面から1m以内の部分にはしるありその他の虫による害を防ぐための措置を講じる(県条例7条)
- ・電気事業法、その他各法令に準じ施工する事。
- ・建築材料の品質は、法第37条に適合させること。
- ・建築物に設ける給水、排水その他配管設備については、「建築設備の構造耐力上安全な構造方法を定める建(平成12年建設省告示第1388号)第5」において、風圧、土圧及び地震その他の震動及び衝撃に対して安全上支障がない構造とする。
- ・下水道法第10条の排水設備の構造の規定に準ずるものとする



一級建築士事務所
アトリエ かなえ

〒901-0405 沖縄県八重瀬町宇伊瀬122-3-A
沖縄県知事登録 第162-3951号 TEL 098-998-1566 / FAX 098-998-1567

一級建築士登録 第 350958 号
漢那 香苗

DWG. DATE
2025/10/23
PRINT. DATE
令和8年 7月16日

検図

製図

縮尺
S=1/100

工事名称

図面名称

儀保様住宅新築工事

1階平面図

施主印

図面番号

A - 104