


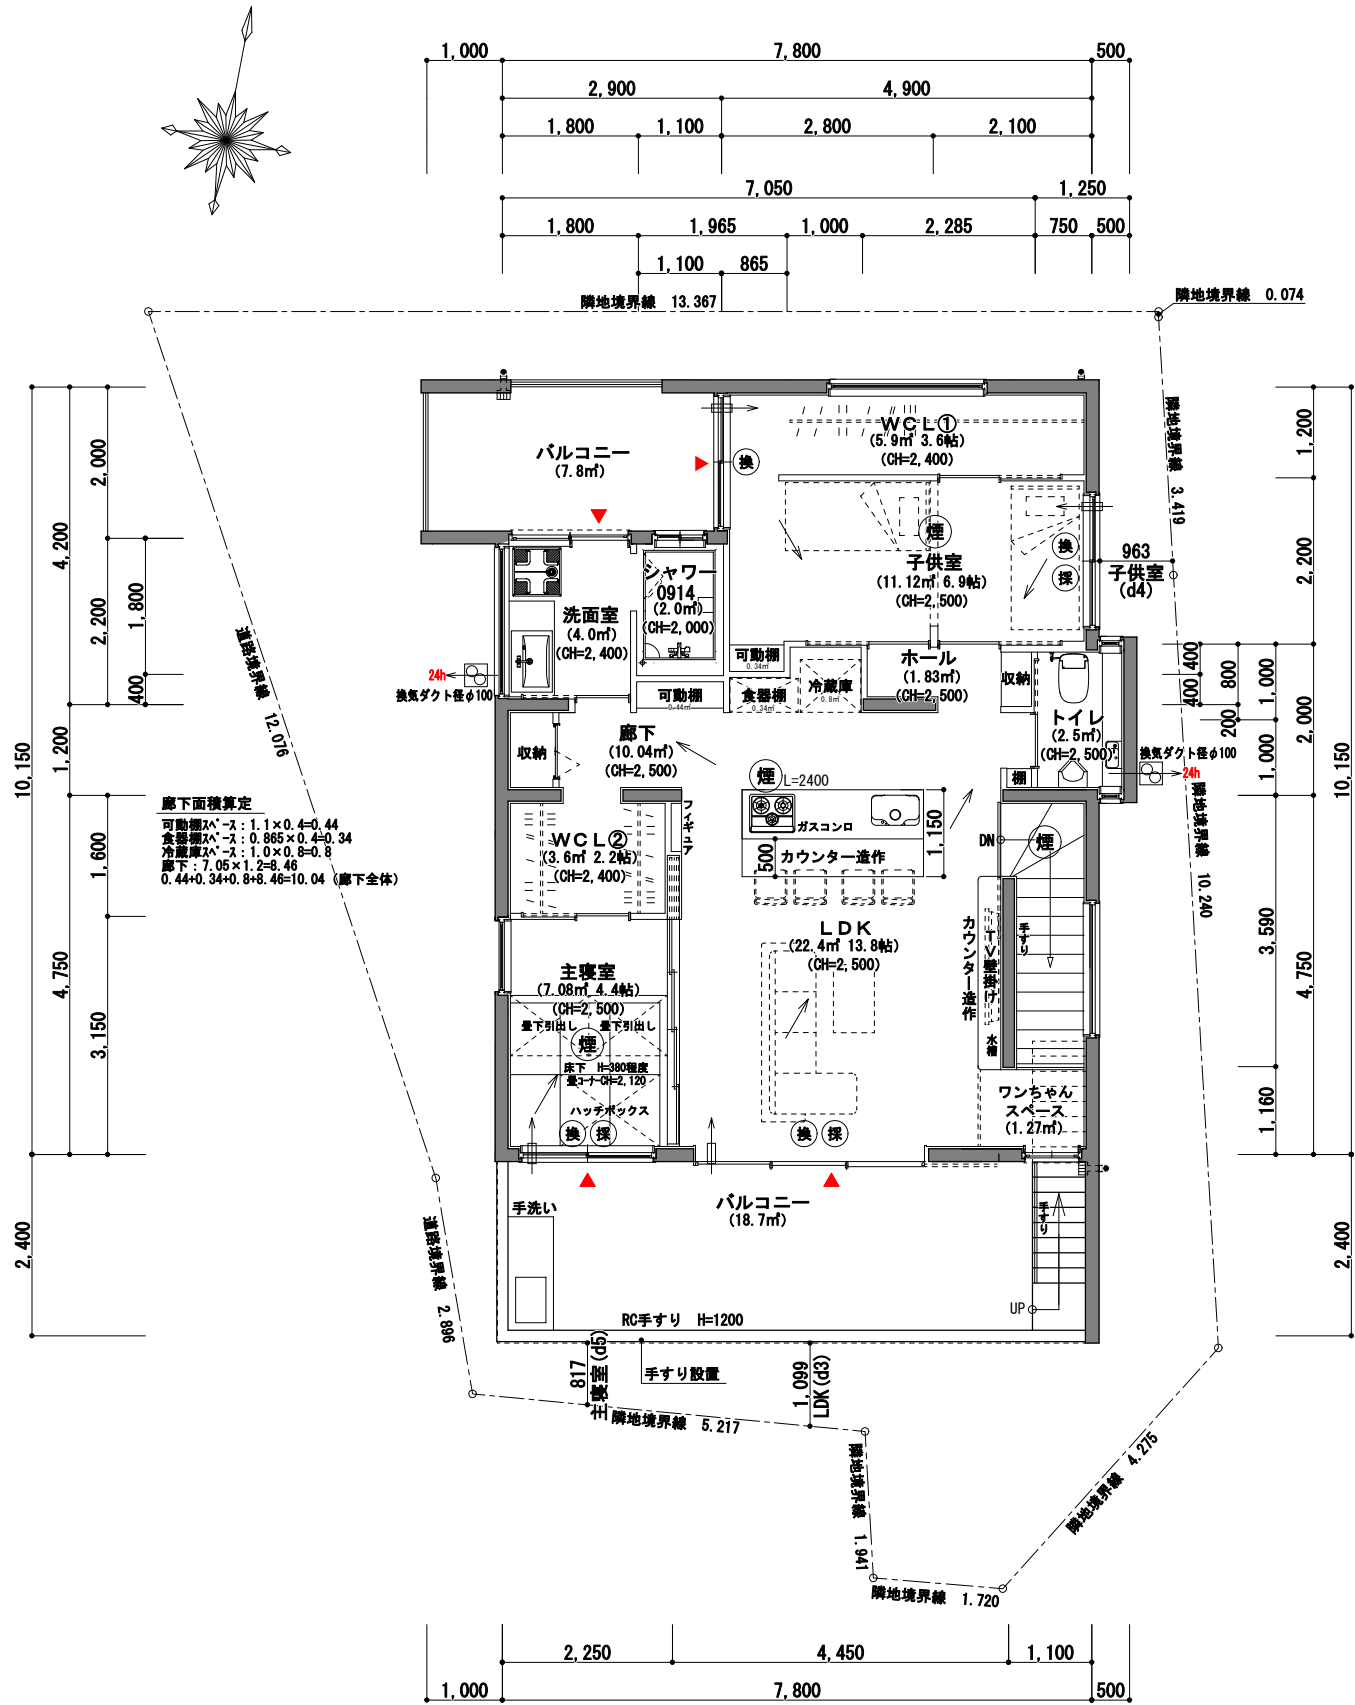

外部階段 (mm)	
蹴上げ	190
踏み面	220
階段幅	700

凡例

- 煙 住宅用火災報知機(煙式)
- 熱 住宅用火災報知機(熱式)
- 換気口
- 換気扇(常時作動) 95m³/h
- 換気経路
- アンダーカット 1cm

採光計算表(2階)

※ワンちゃんスペース: 1.1 * 1.16 = 1.27 m ²										※可動棚スペース: 0.865 * 0.4 = 0.34 m ²																		
室名		LDK						子供室						主寝室														
居室の床面積		4450	×	4750	=	2113	m ²	21.13+1.27=	22.4	4900	×	2200	=	1078	m ²	10.78+0.34=	11.12	2250	×	3150	=	708	m ²					
必要採光面積		22.4	/	7.00	=	3.2	m ²			11.12	/	7.00	=	1.58	m ²			7.08	/	7.00	=	1.01	m ²					
必要補正係数	水平距離 D3=		1.089		A=		2.26			水平距離 D4=		0.963		A=		3.00			水平距離 D5=		0.817		A=		1.64			
	垂直距離 H3=		1.8							垂直距離 H4=		1.2							垂直距離 H5=		1.61							
		1.099	/	1.8	×	6	-	1.4	=	2.26	0.963	/	1.2	×	6	-	1.4	=	3.41	0.817	/	1.61	×	6	-	1.4	=	1.64
建具①		3.00	×	2.30	=	6.9	m ²			1.70	×	2.0	=	3.4	m ²			1.70	×	1.92	=	3.26	m ²					
建具②										1.70	×	0.5	=	0.85	m ²													
有効採光面積		2.26	×	6.9	=	1559	m ²			3.00	×	0.85	=	255	m ²			1.64	×	3.26	=	534	m ²					
判定		1559	≥	32	…	OK				255	≥	158	…	OK			534	≥	1.01	…	OK							

※採光は建具②のみで算定

換気計算表(2階)

室 名	LDK						子供室						主寝室					
必要換気面積	22.40	/	20	=	1.12	m²	11.12	/	20	=	0.55	m²	7.08	/	20	=	0.35	m²
有効換気面積①	6.9	/	2	=	3.45	m²	3.4	/	2	=	1.70	m²	3.26	/	2	=	1.63	m²
有効換気面積②							0.85	/	2	=	0.42	m²	①+② =		2.12			
判 定	3.45	≧	1.12	…	OK		2.12	≧	0.55	…	OK		1.63	≧	0.35	…	OK	



一級建築士事務所
アトリエ かやえ

〒901-0405 沖縄県八重瀬町字伊瀬122-3-A
沖縄県知事登録 第162-3951号 TEL 098-998-1566 / FAX 098-998-1567

一級建築士登録 第 350958 号
漢那 香苗

DWG. DATE
2025/10/23
PRINT. DATE
令和8年 7月16日

検図

製図

縮尺
S=1/100

工事名称

図面名称

儀保様住宅新築工事

2階平面図

施主印

図面番号

A - 105