
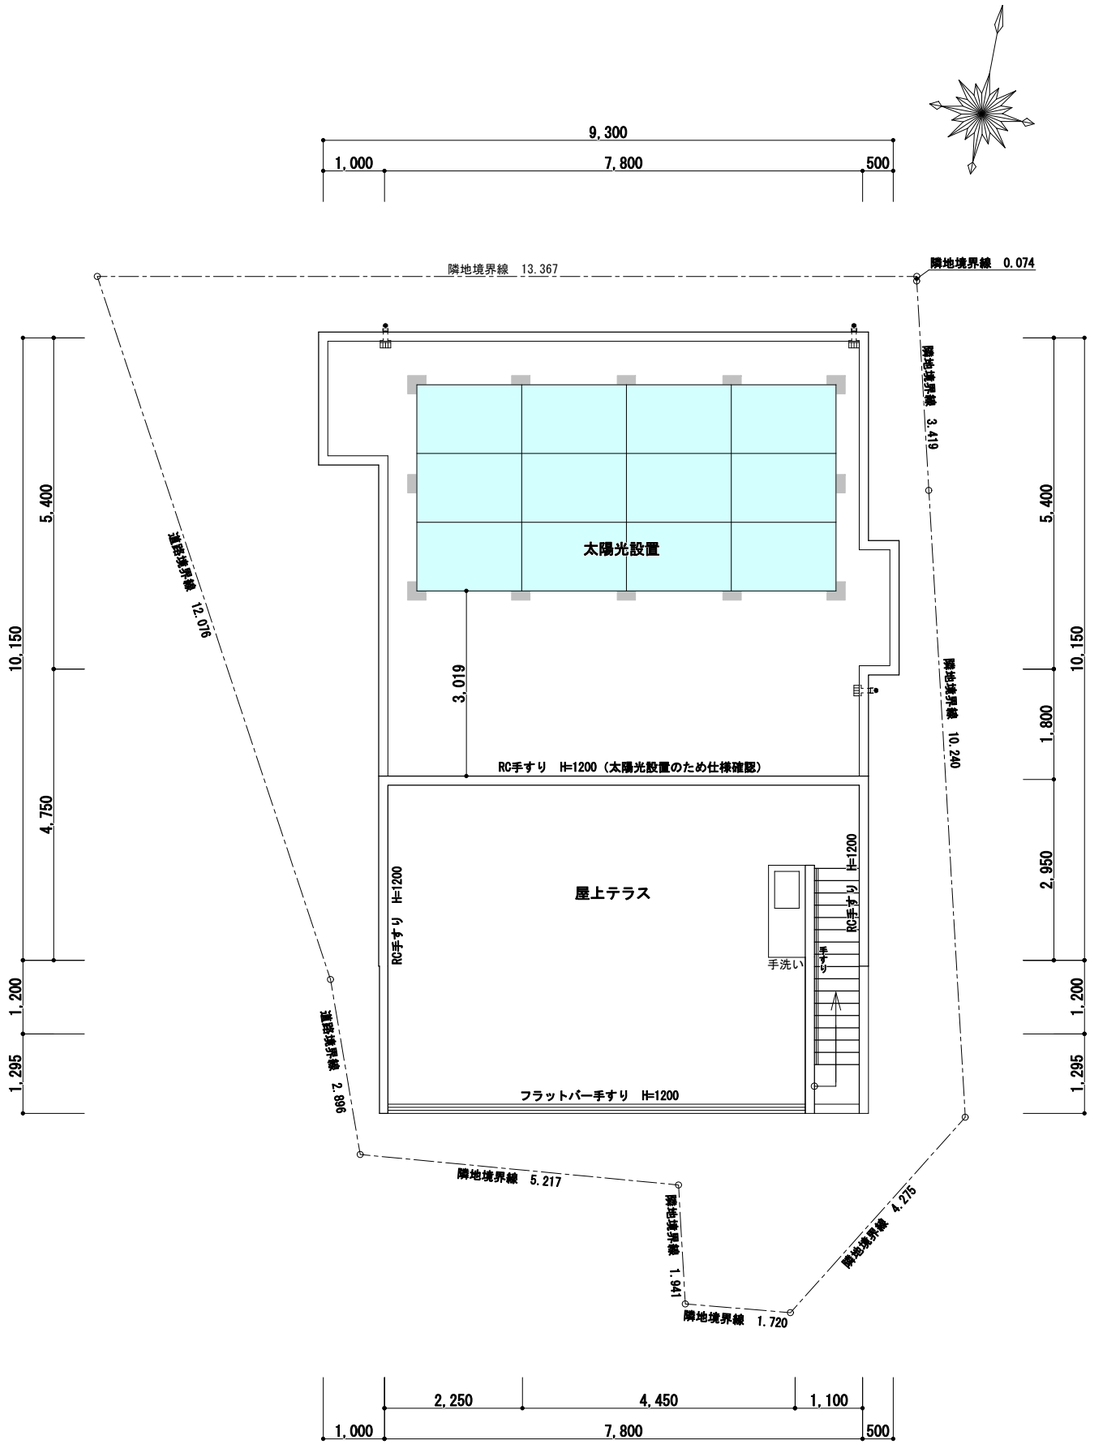


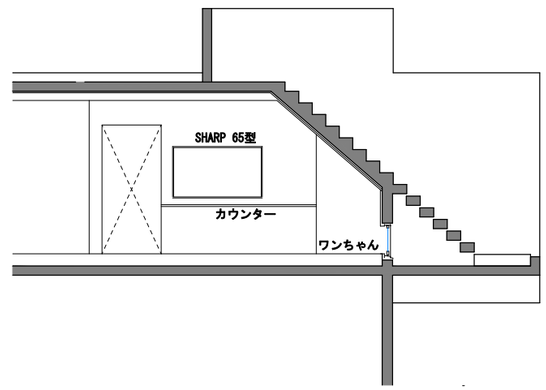

外部階段(mm)	
蹴上げ	190
踏み面	220
階段幅	700

凡例

- 煙 住宅用火災報知機(煙式)
- 熱 住宅用火災報知機(熱式)
- 換気口
- 換気扇(常時作動) 95m³/h
- 換気経路
- アンダーカット 1cm

一級建築士事務所
アトリエ かなえ
〒901-0405 沖縄県八重瀬町字伊覇122-3-A
沖縄県知事登録 第162-3951号 TEL 098-998-1566 / FAX 098-998-1567

一級建築士登録 第 350958 号
漢那 香苗

DWG. DATE	検図	製図	縮尺	工事名称	儀保様住宅新築工事	施主印	図面番号
2025/10/22			S=1/100	図面名称	R階平面図		A - 106
PRINT. DATE 令和8年 7月16日							