



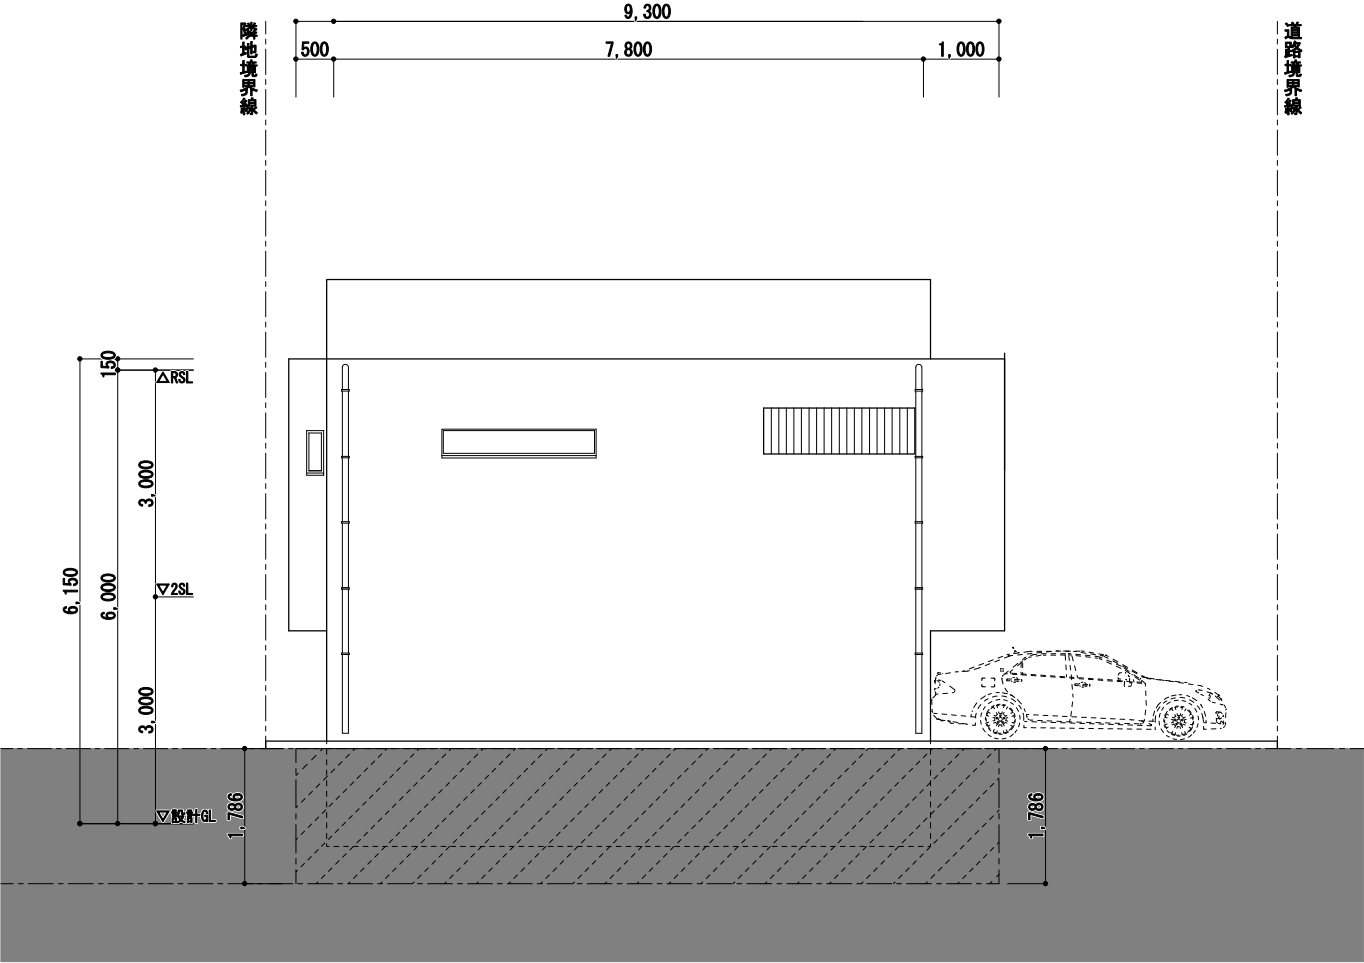

北側立面図 S=1/100

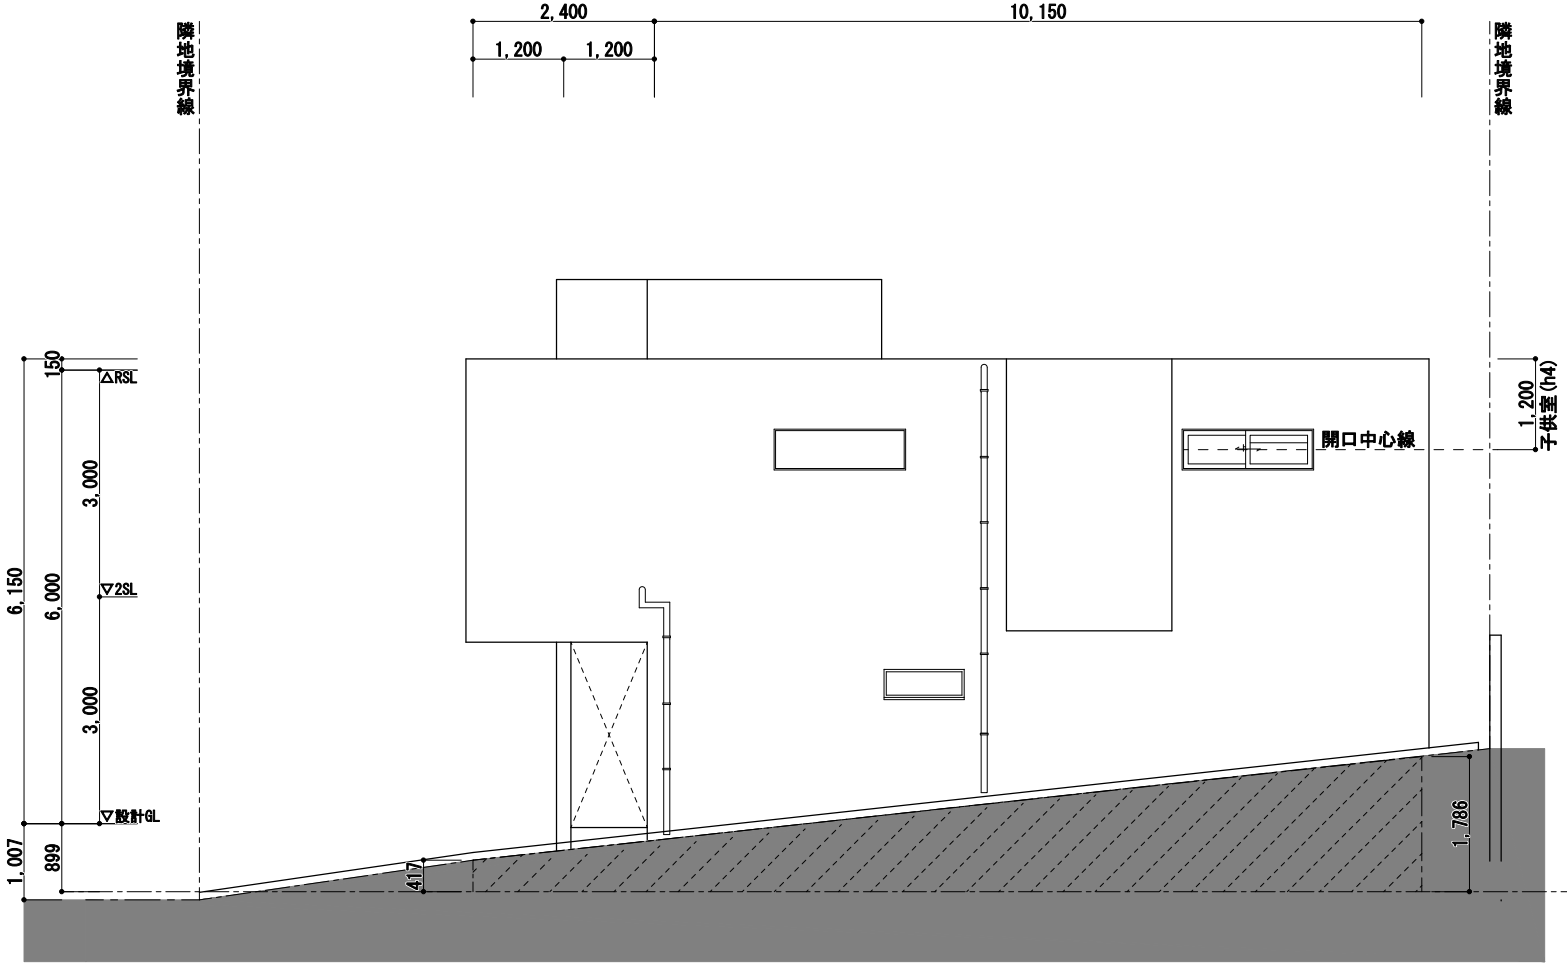

東側立面図 S=1/100

前面道路斜線制限の算定 セットバック距離 道路幅員 (0.00 + 4.000) × 1.25 = 5.000
北側斜線制限の算定 立上り高さ (10.000) × 1.25 = 12.500
隣地境界線斜線制限の算定 立上り高さ (20.000) × 1.25 = 25.000

※北側・道路斜線・隣地斜線適合している。