



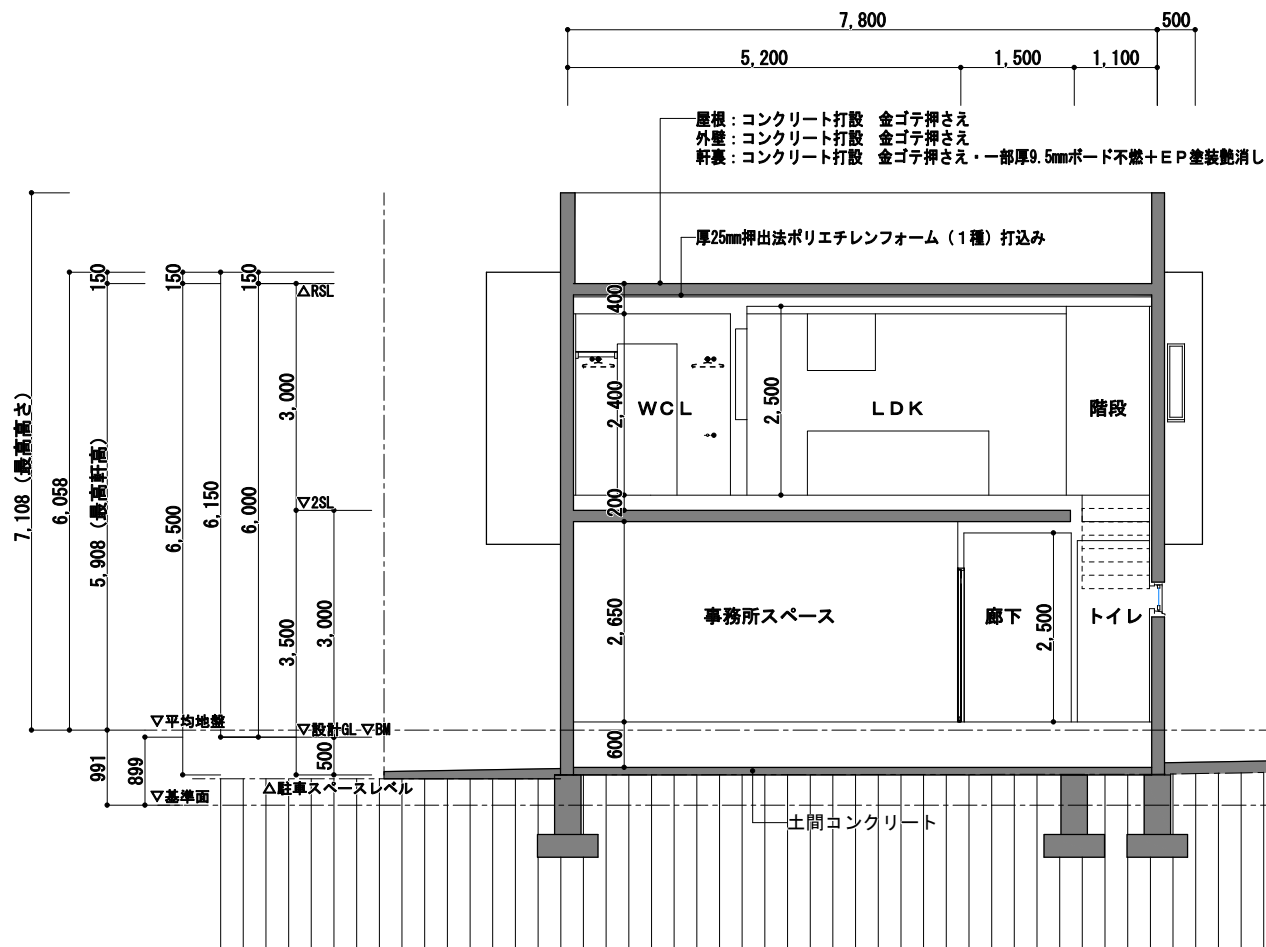

A-A断面図 S=1/100



B-B断面図 S=1/100

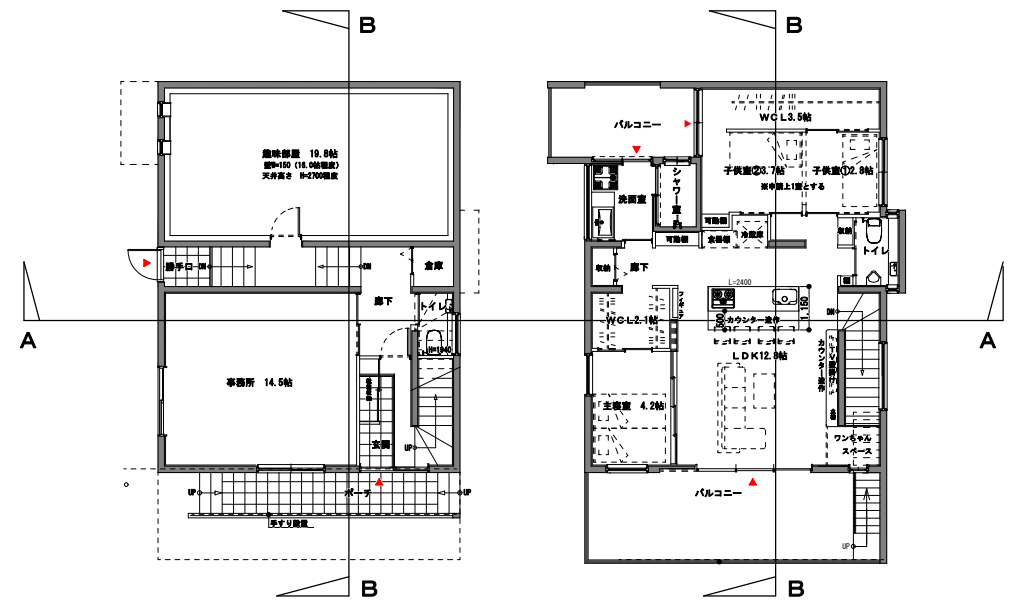

一級建築士事務所
アトリエ かなえ

〒901-0405 沖縄県八重瀬町宇伊瀬122-3-A
沖縄県知事登録 第162-3951号 TEL 098-998-1566 / FAX 098-998-1567

一級建築士登録 第 350958 号
漢那 香苗

DWG. DATE
2025/11/07
PRINT. DATE
令和8年 7月16日

検図

製図

縮尺
S=1/100

工事名称
図面名称

儀保様住宅新築工事
断面図

施主印

図面番号

A - 109