


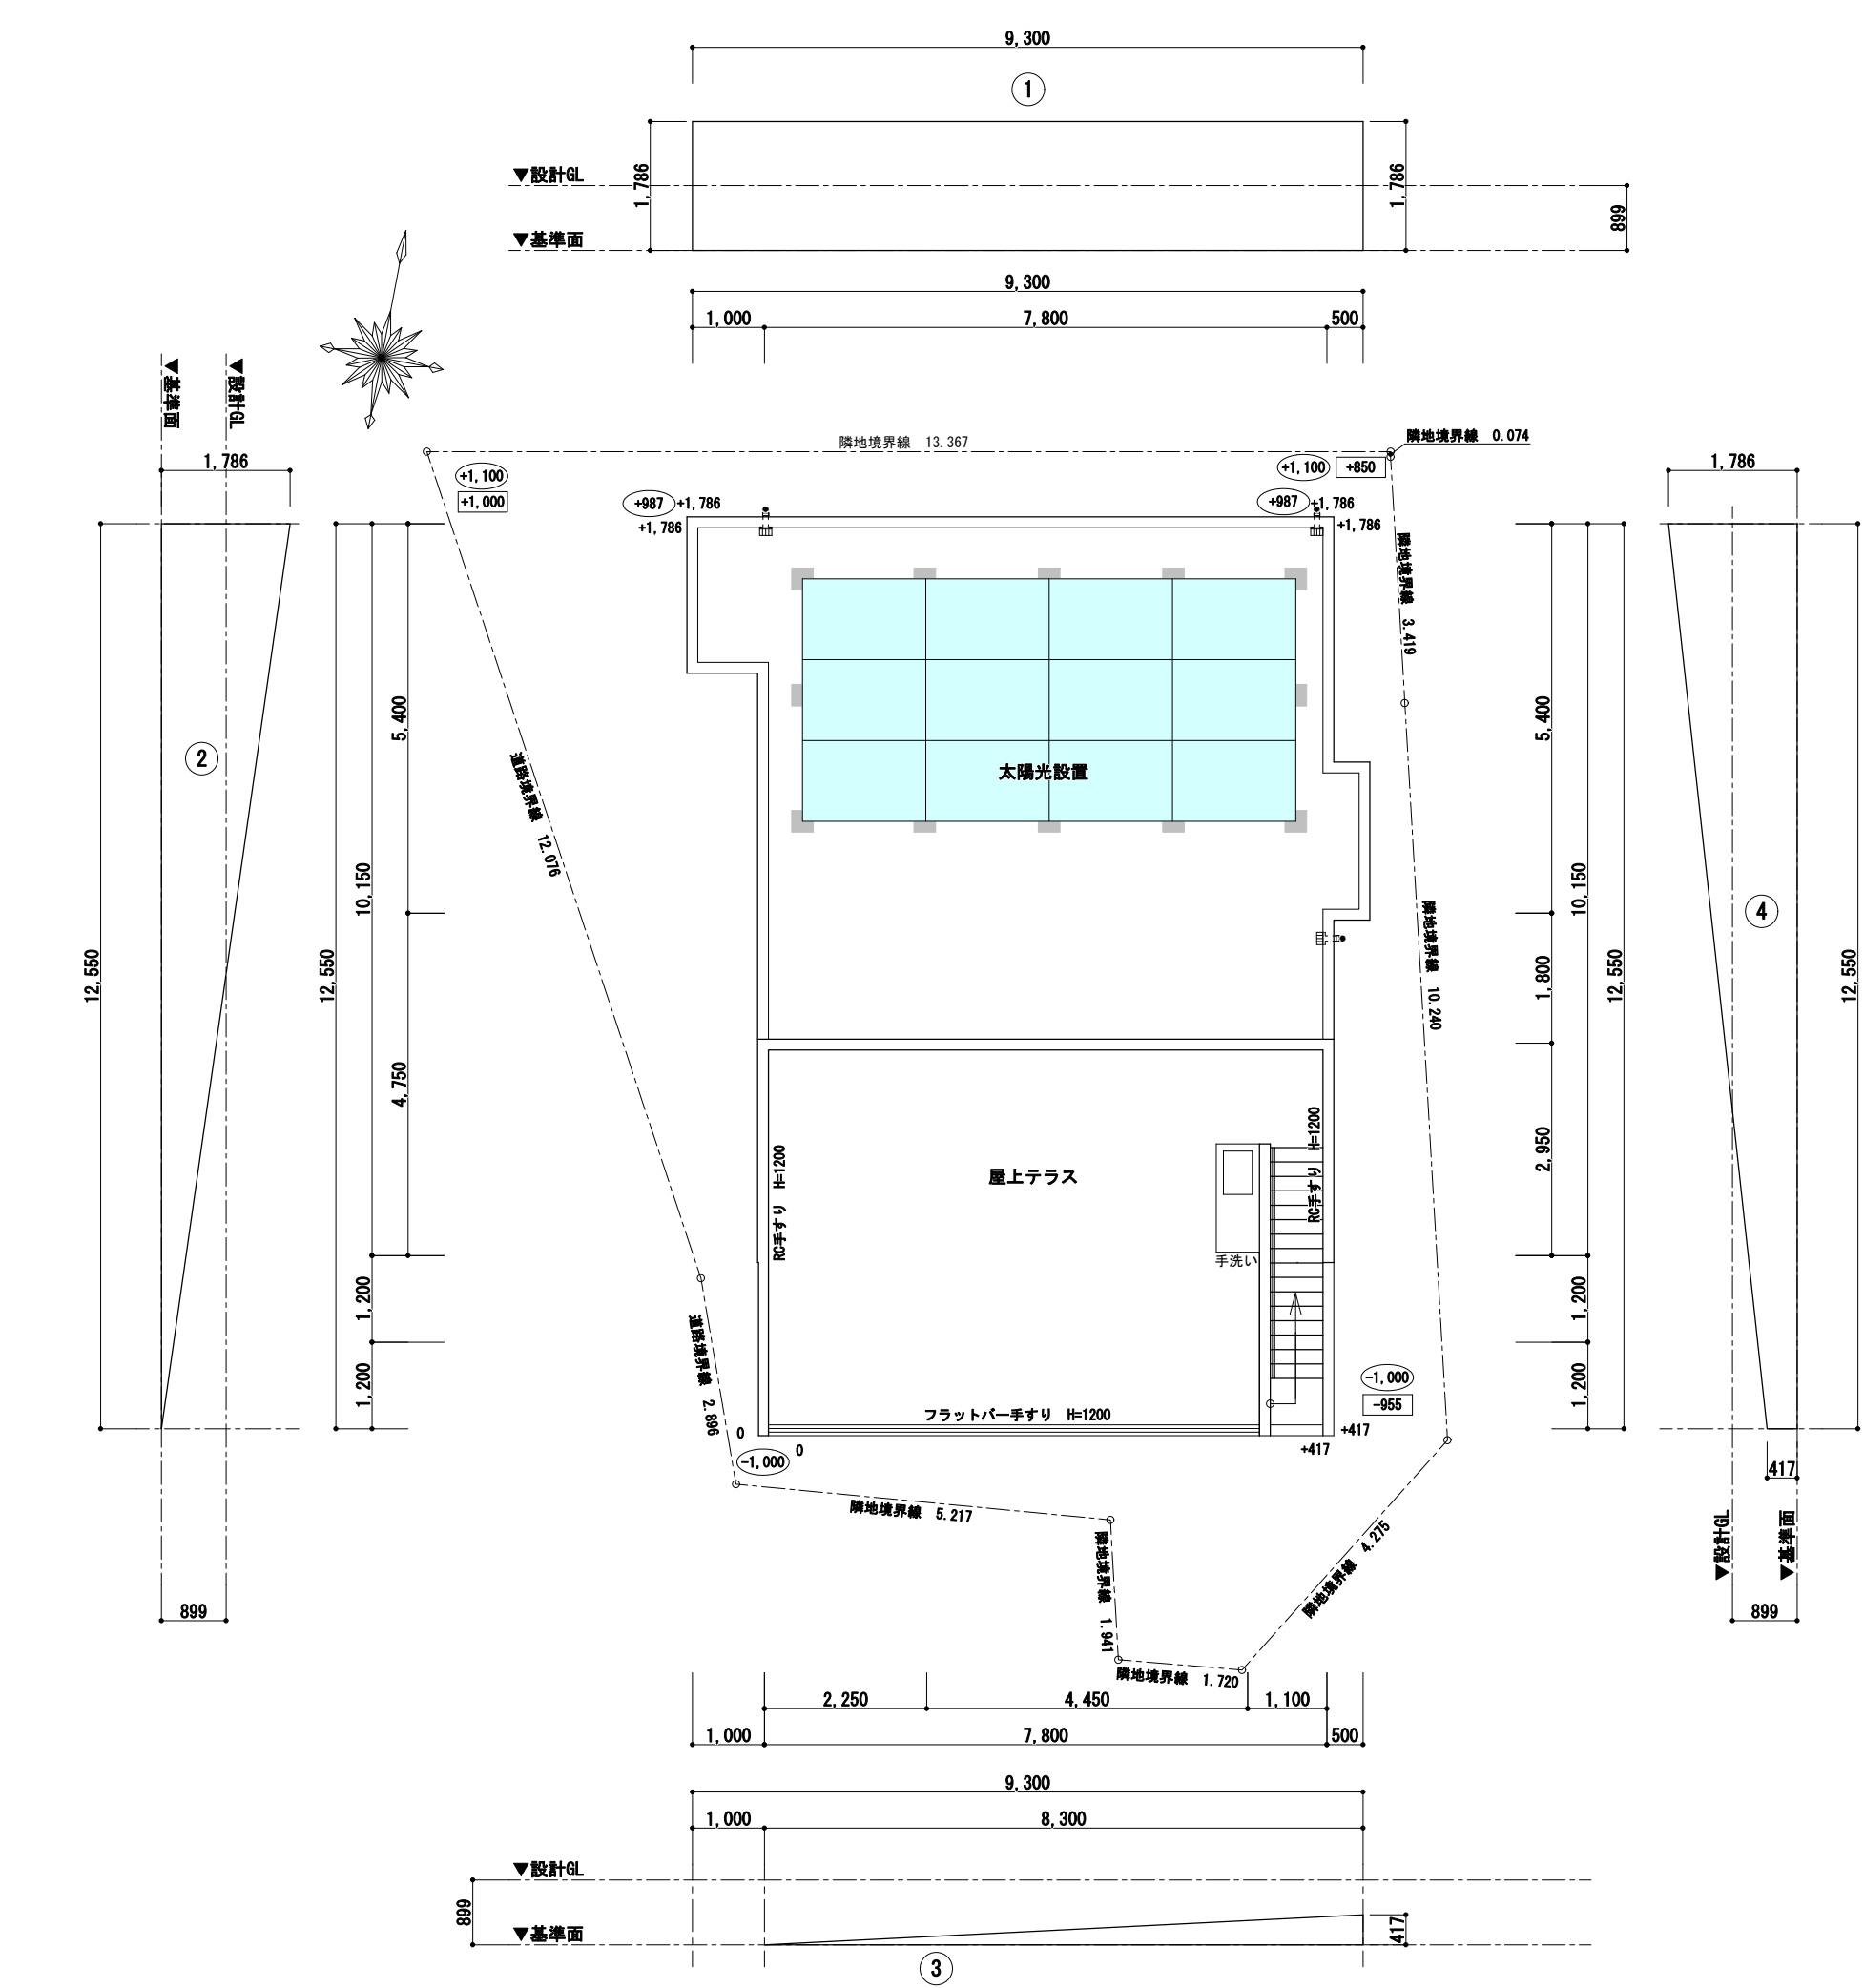

平均地盤面算定表 S=1/100

①	9.300	*	1.786	=	16.600
②	12.550	*	1.786	* 0.5 =	11.200
③	8.300	*	0.417	* 0.5 =	1.730
④	(0.417 + 1.786)	*	12.55	* 0.5 =	13.820

建物周長 43.70 合計面積 43.350

平均地盤 43.350 / 43.70 = **0.991**

周長計算①

9.300
12.550
9.300
12.550

43.700

現況レベル

設計計画レベル