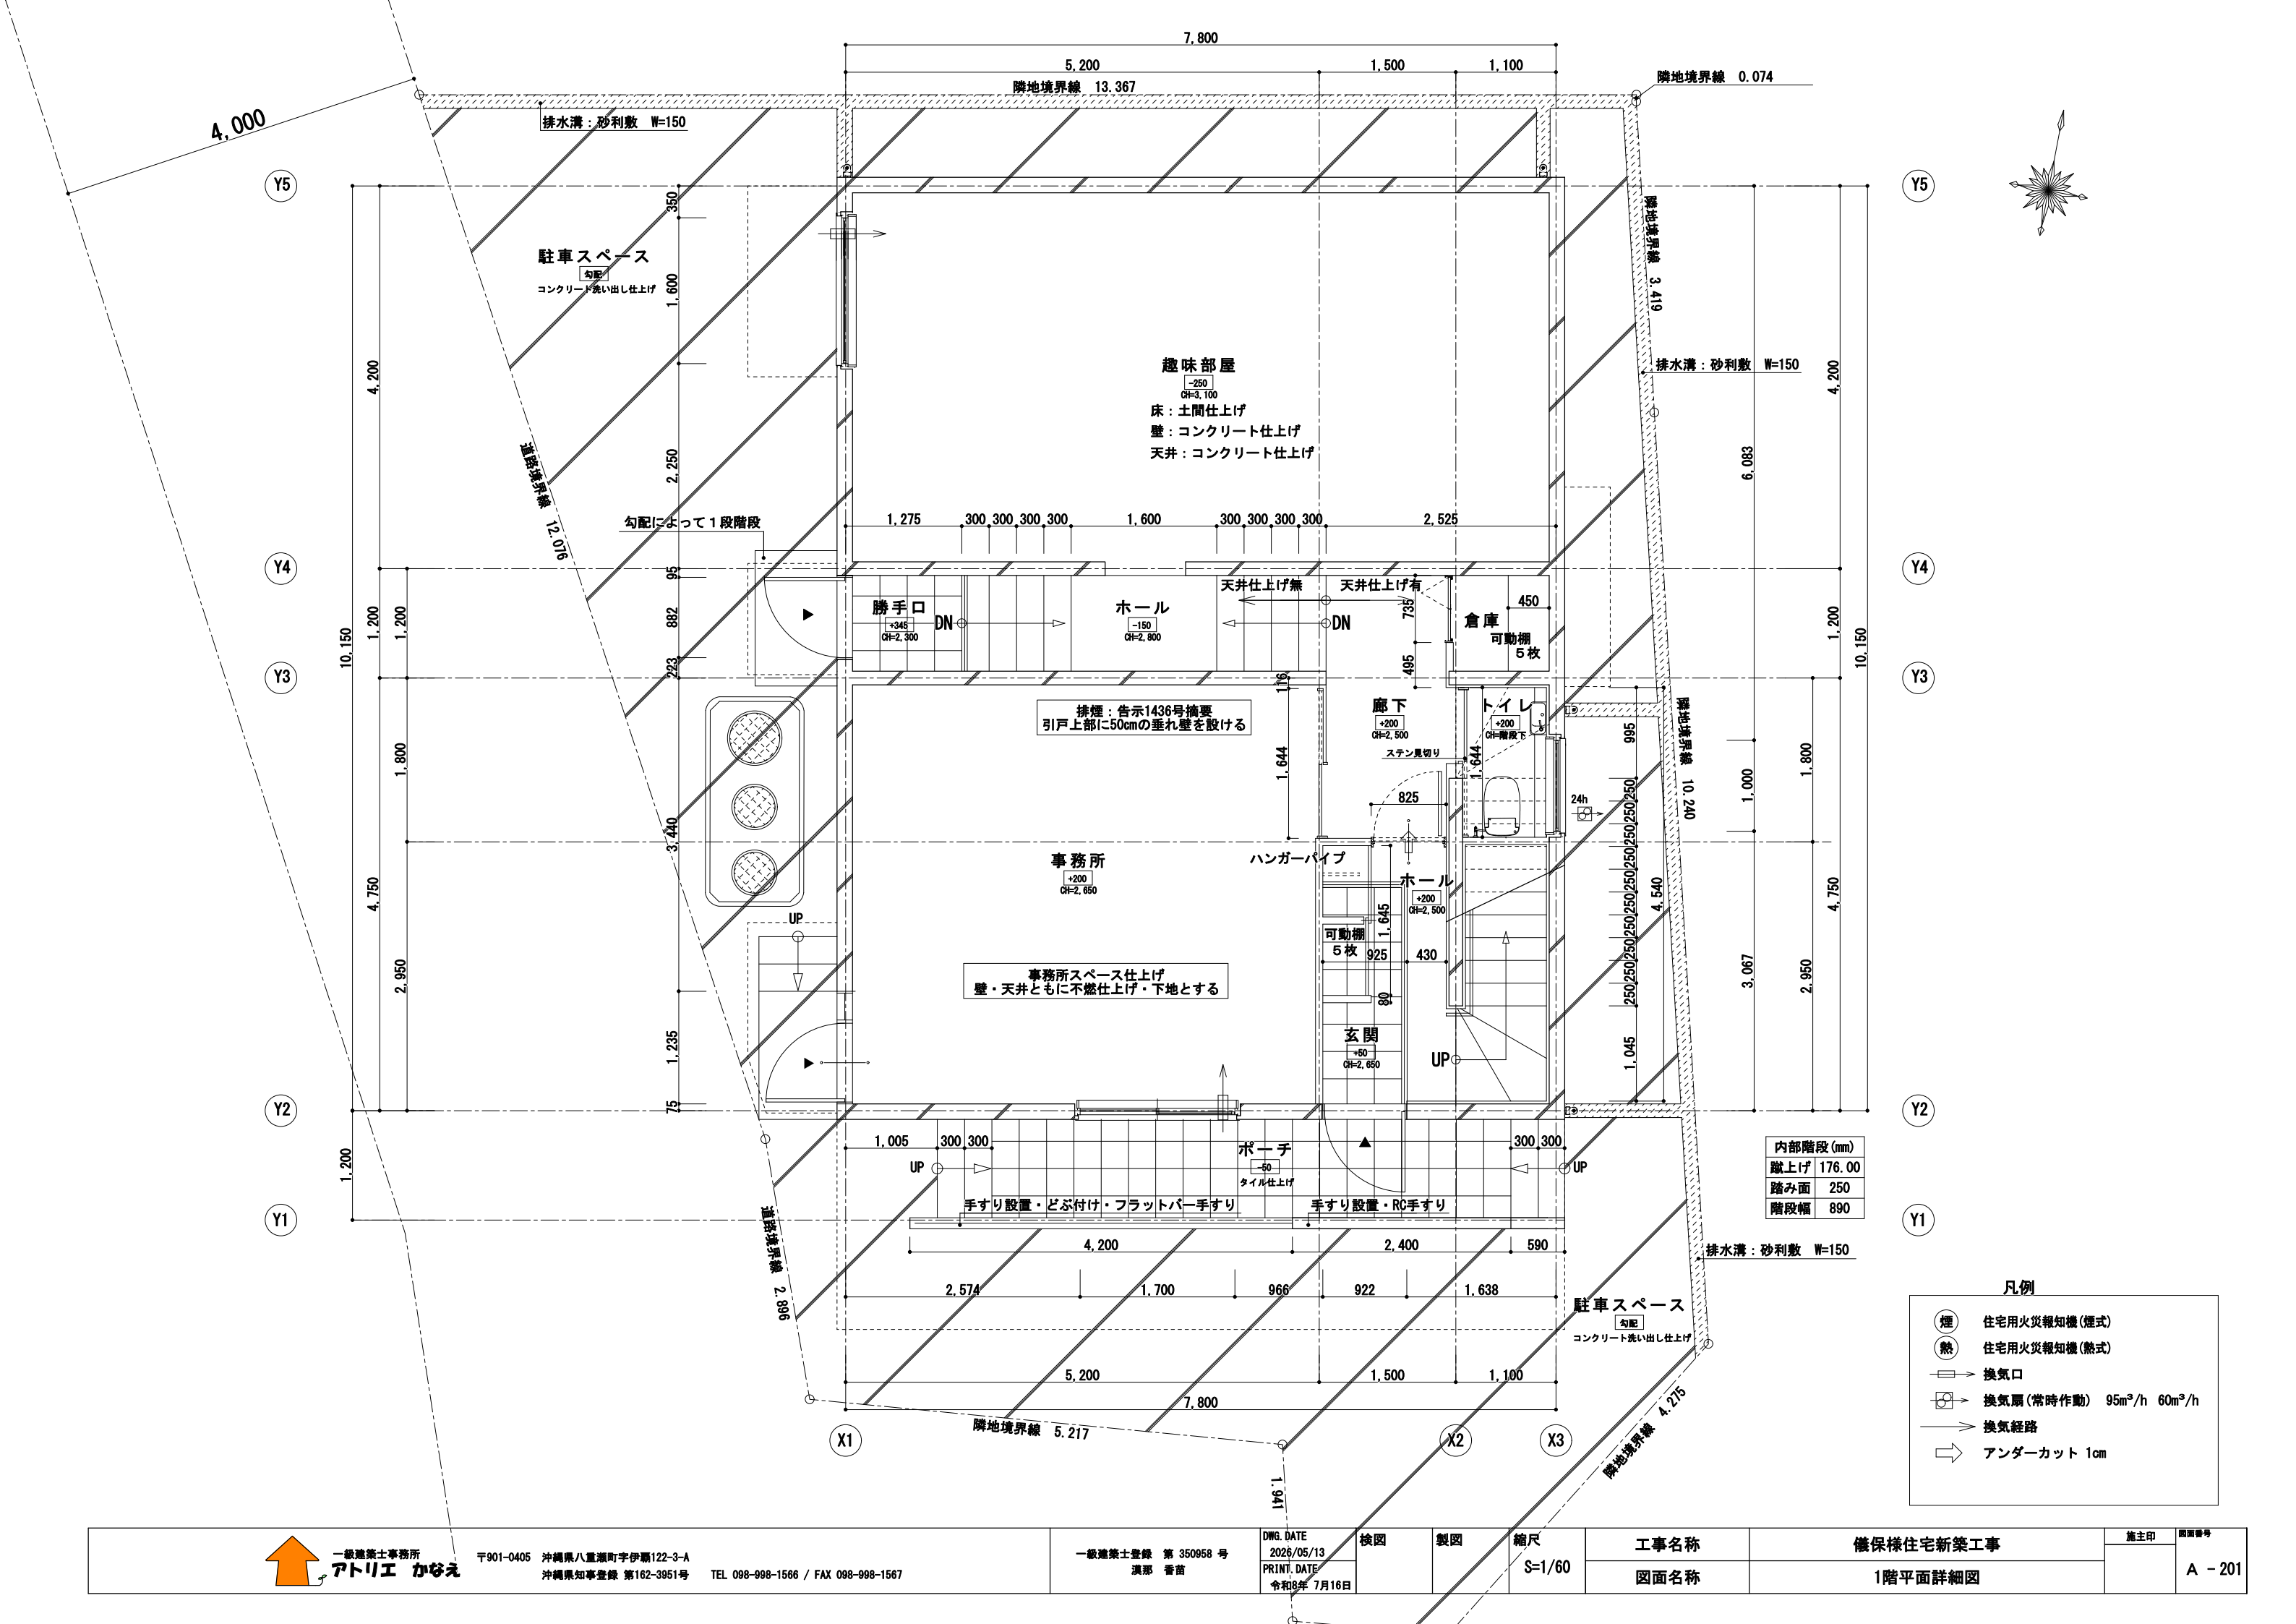


- 凡例
- 煙 住宅用火災報知機(煙式)
 - 熱 住宅用火災報知機(熱式)
 - 換気口
 - 換気扇(常時作動) 95m³/h 60m³/h
 - 換気経路
 - アンダーカット 1cm