


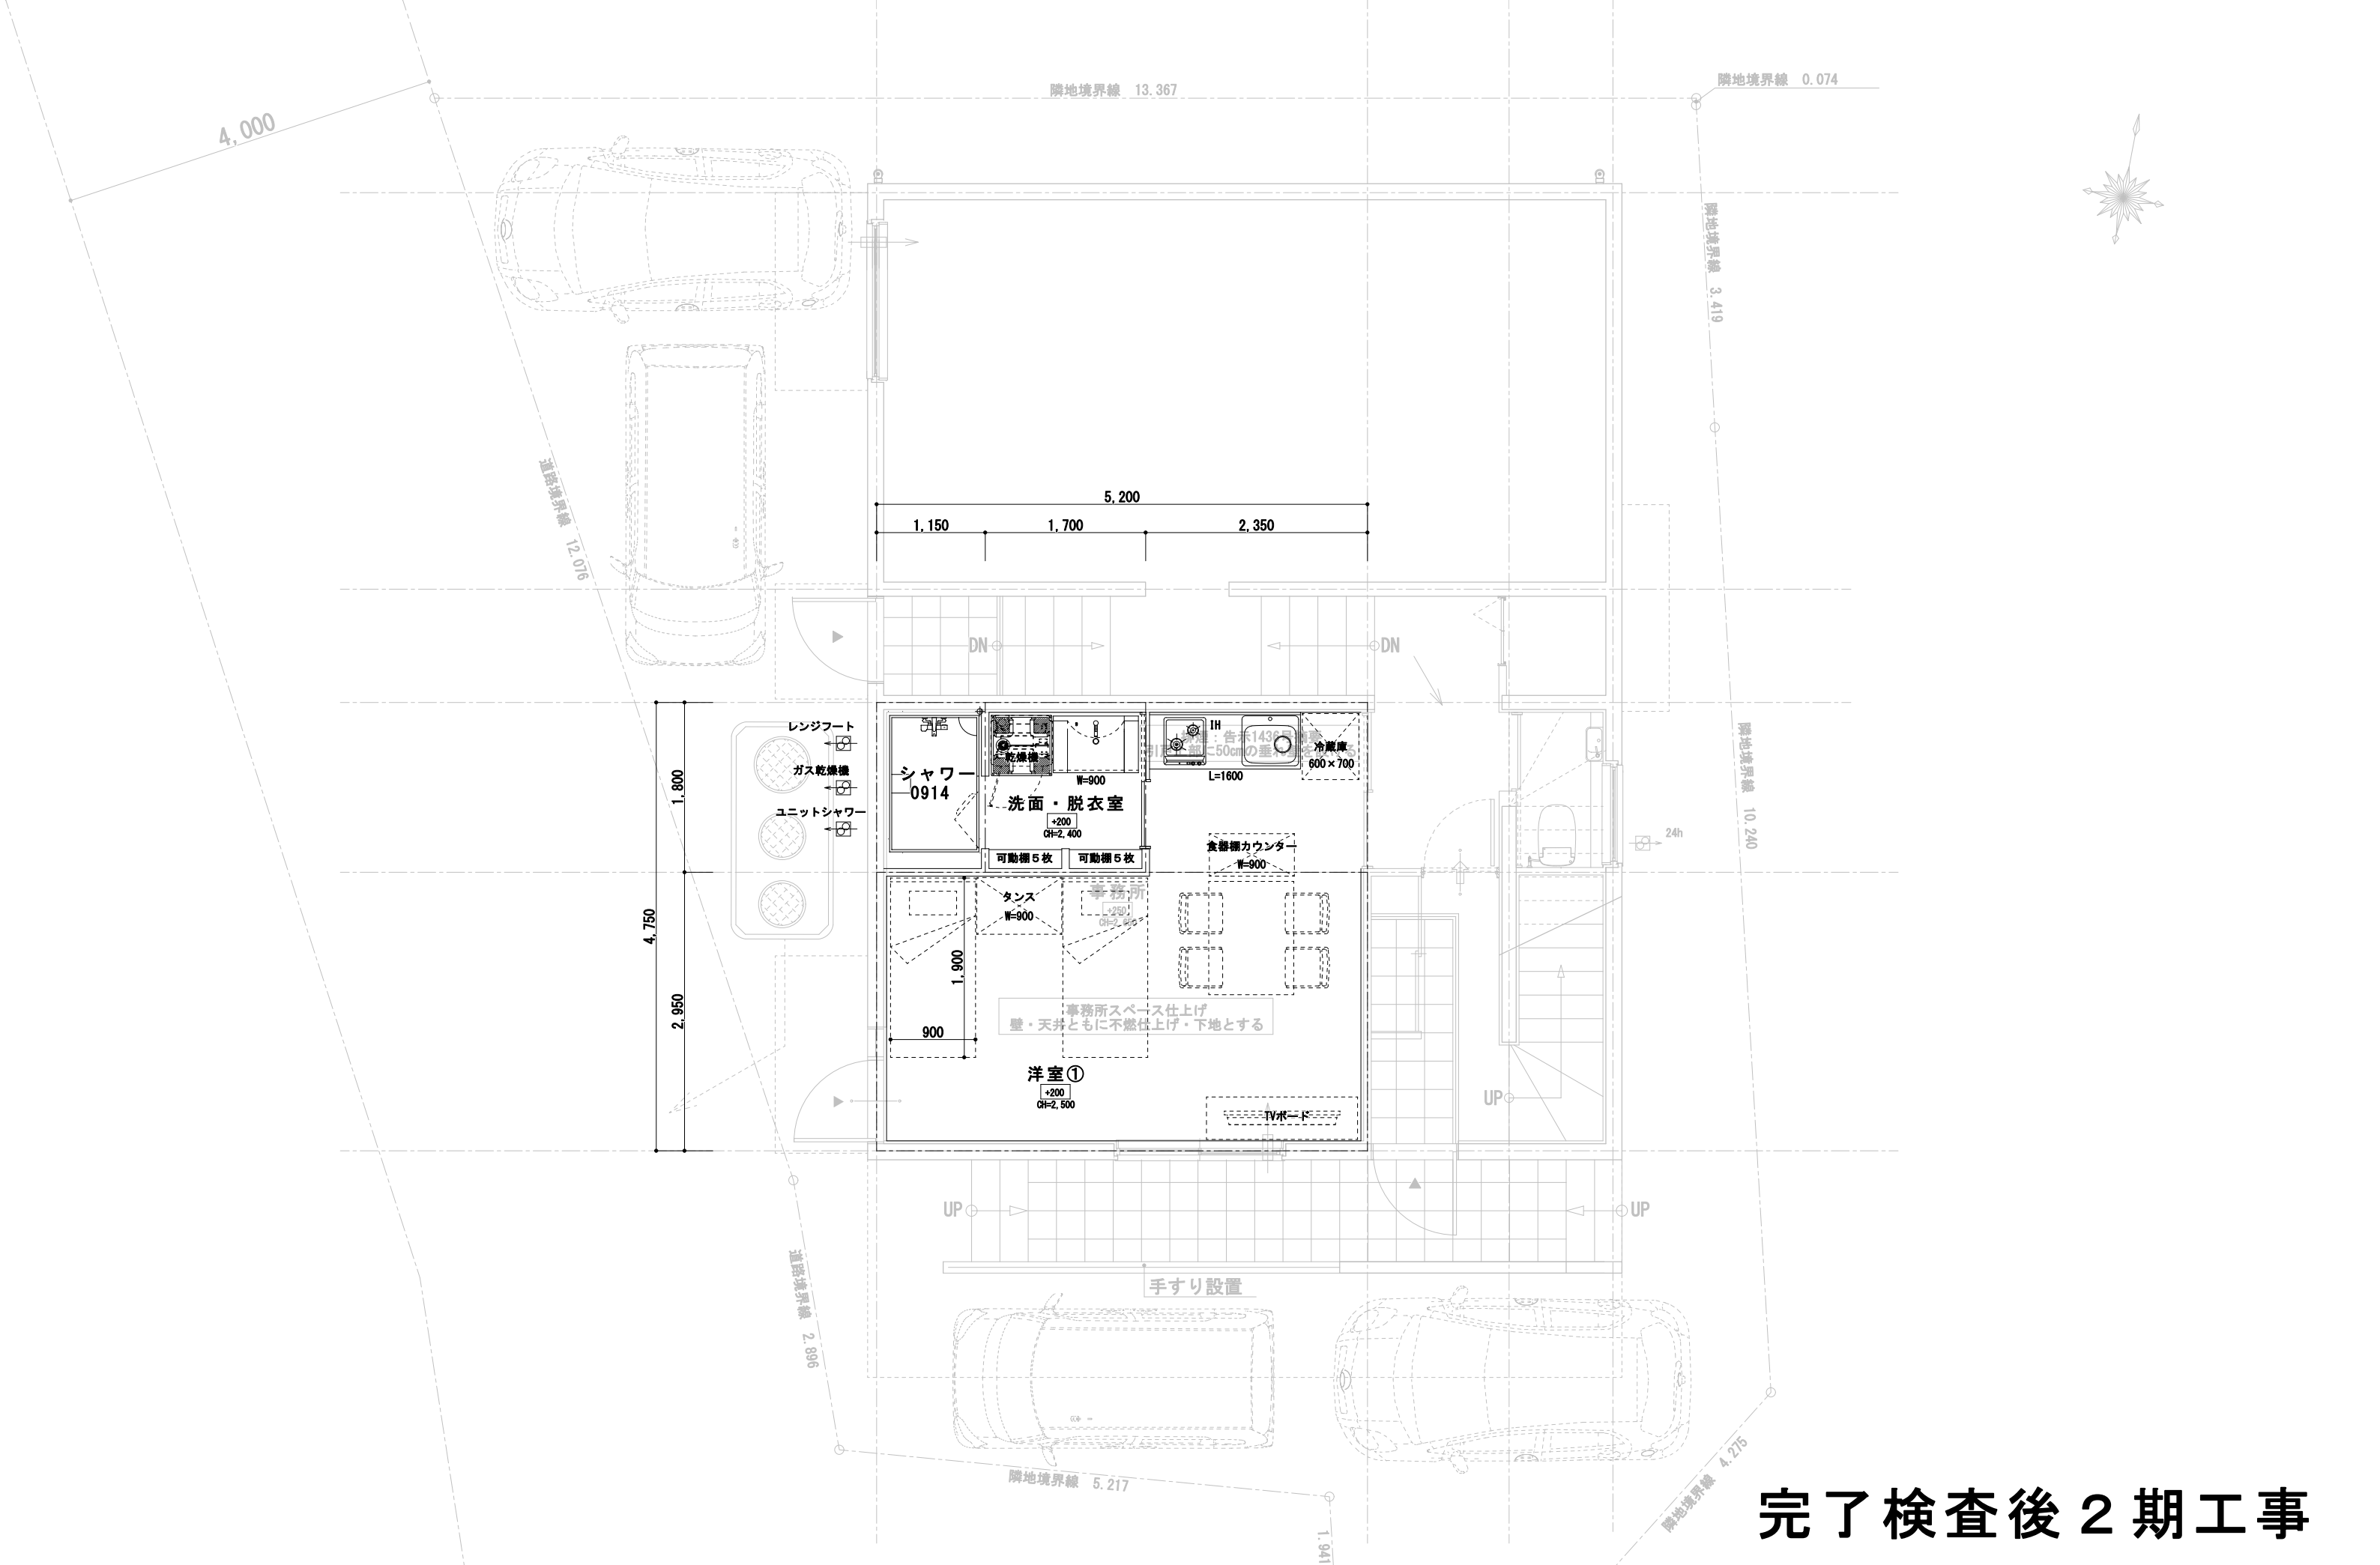

完了検査後 2 期工事

 一級建築士事務所 アトリエ かなえ	〒901-0405 沖縄県八重瀬町宇伊覇122-3-A 沖縄県知事登録 第162-3951号 TEL 098-998-1566 / FAX 098-998-1567	一級建築士登録 第 350958 号 渡那 香苗	DWG. DATE 2026/05/13 PRINT. DATE 令和8年 7月16日	検図	製図	縮尺 S=1/60	工事名称	儀保様住宅新築工事（2期工事）	施主印	図面番号 A -201a
							図面名称	1階平面詳細図		