A
D 展開方向 B
C

室名	子供室①②
床	厚12mmラワン合板＋ Panasonic床材
巾木	Panasonic巾木　同等品 (H=3.0)
壁	厚12.5mmＰＢ下地 ビニールクロス仕上(ベスト1000)同等品
天井	厚9.5mmＰＢ下地 ビニールクロス仕上(ベスト1000)同等品

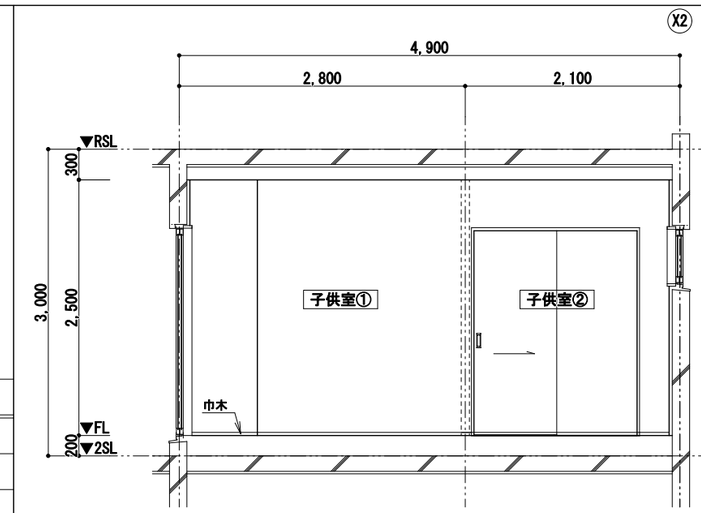

A方向

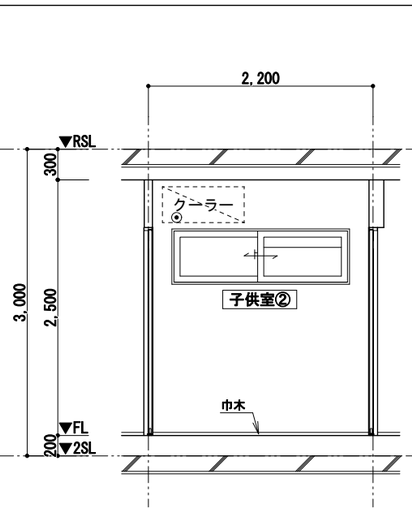

B方向

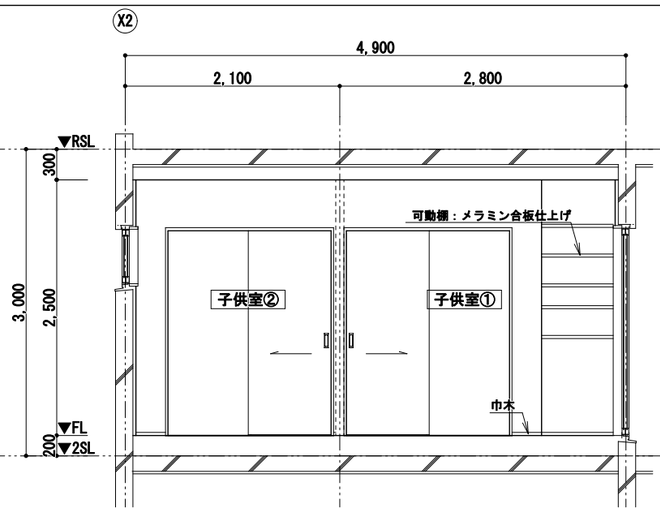

C方向

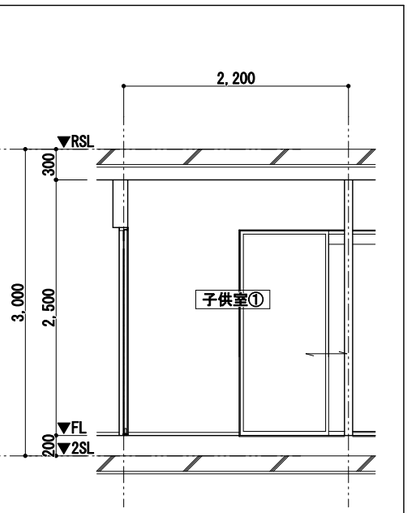

D方向

A
D 展開方向 B
C

室名	WCL①
床	厚12mmラワン合板＋ Panasonic床材
巾木	Panasonic巾木　同等品 (H=3.0)
壁	厚12.5mmＰＢ下地 ビニールクロス仕上(ベスト1000)同等品
天井	厚9.5mmＰＢ下地 ビニールクロス仕上(ベスト1000)同等品

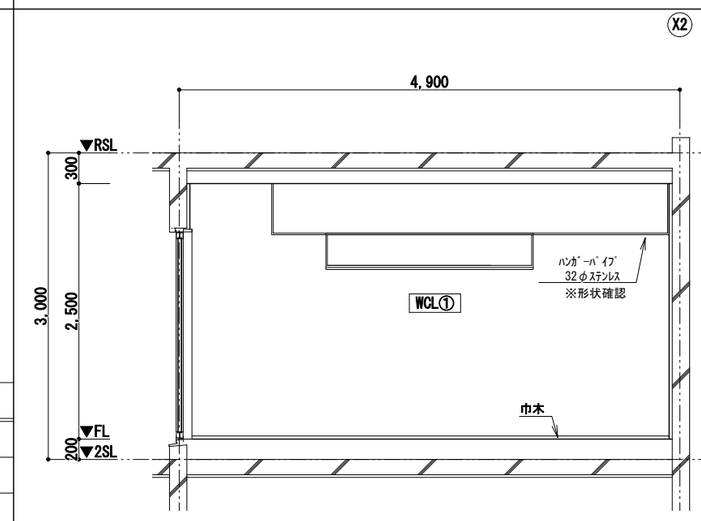

A方向

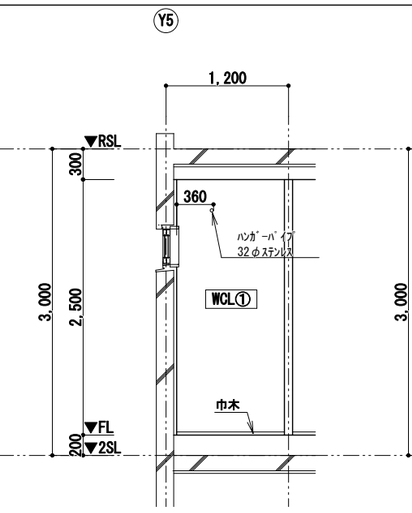

B方向

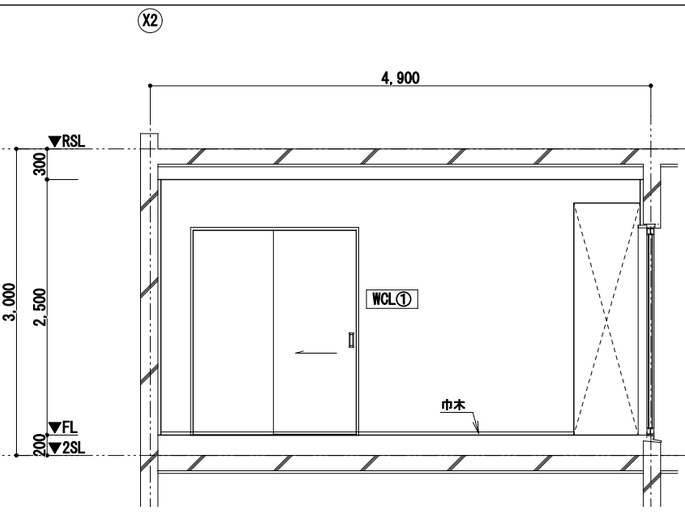

C方向

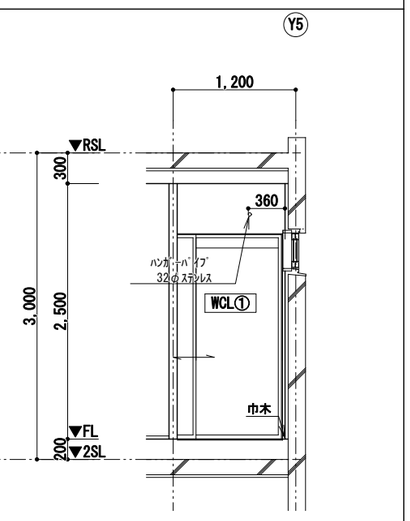

D方向

A
D 展開方向 B
C

室名	WCL②
床	厚12mmラワン合板＋ Panasonic床材
巾木	Panasonic巾木　同等品 (H=3.0)
壁	厚12.5mmＰＢ下地 ビニールクロス仕上(ベスト1000)同等品
天井	厚9.5mmＰＢ下地 ビニールクロス仕上(ベスト1000)同等品

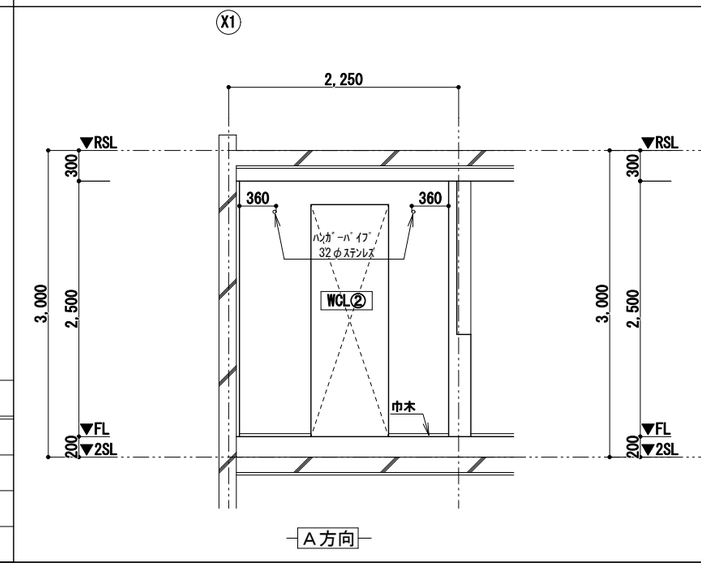

A方向

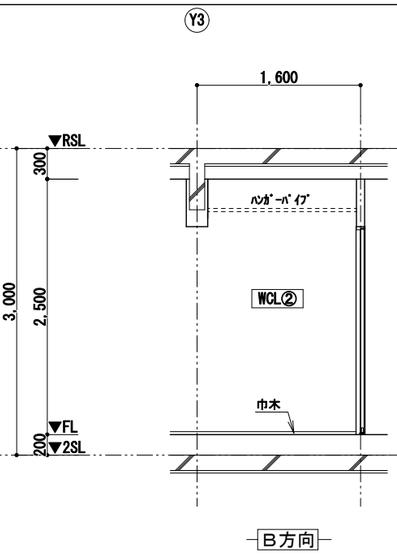

B方向

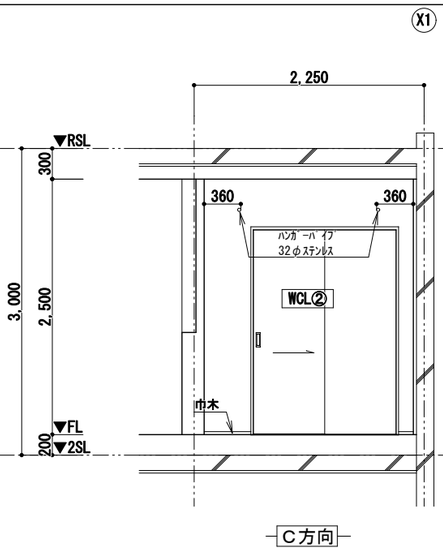

C方向

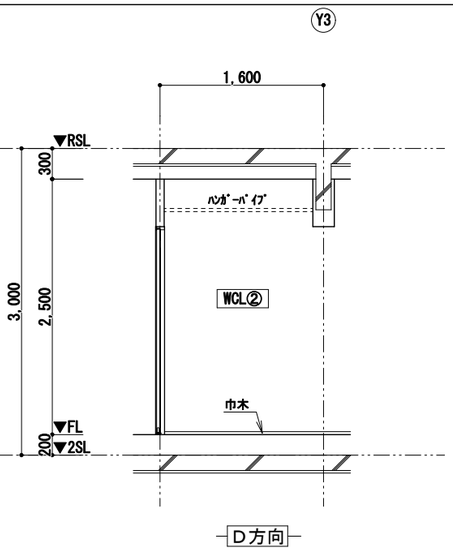

D方向

一級建築士事務所
アトリエ　かなえ
〒901-0405　沖縄県八重瀬町字伊覇122-3-A
沖縄県知事登録 第162-3951号　TEL 098-998-1566 / FAX 098-998-1567

一級建築士登録　第 350958 号
漢那　香苗

DWG. DATE	検図	製図	縮尺	工事名称	儀保様住宅新築工事	施主印	図面番号
2026/06/03			S=1/60	図面名称	2階展開図②		A - 205
PRINT. DATE 令和8年 7月16日							